RD Šíma · 1.NP · skladby podlah pro řemesla

A3 · 1:125 · +Y sever · tloušťky z podlaha-eps.xlsx

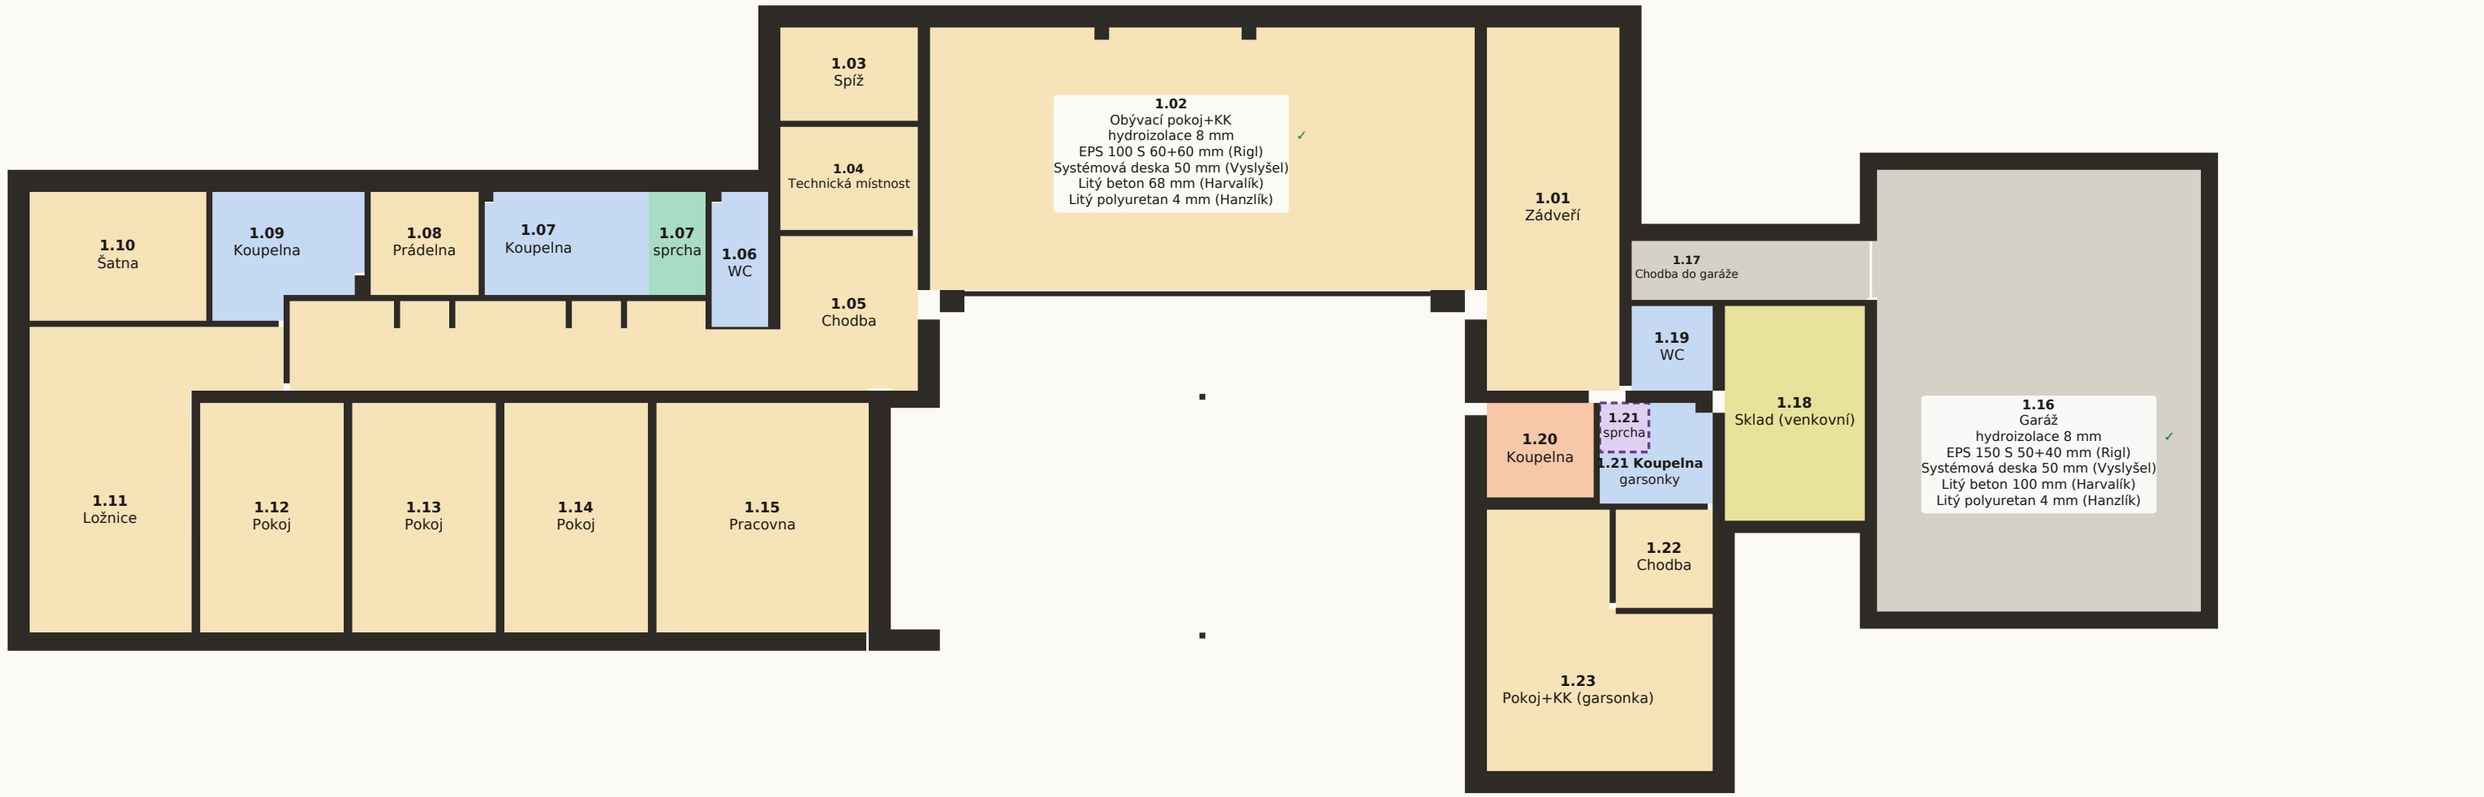

Legenda

Dům — litý polyuretan · Dlažba, potěr Harvalík · 1.20 celá ve spádu, potěr Harvalík · Sprcha 1.07, potěr Doskočil · Sprcha 1.21, 1×1 m, předpoklad · Garáž a chodba 1.17 — EPS 150 S · Sklad 1.18 — bez systémové desky

Dlažba, potěr Harvalík
hydroizolace 8 mm ✓
EPS 100 S 60+60 mm (Rigl)
Systémová deska 50 mm (Vyslyšel)
Litý beton 59 mm (Harvalík)
hydroizolace + lepidlo + dlažba 13 mm (Doskočil)

1.20 celá ve spádu, potěr Harvalík
hydroizolace 8 mm ✓
EPS 100 S 40+40 mm (Rigl)
Systémová deska 50 mm (Vyslyšel)
Litý beton 99 mm u nuly / 56 mm u vpusti (Harvalík)
hydroizolace + lepidlo + dlažba 13 mm (Doskočil)

Sprcha 1.07, potěr Doskočil
hydroizolace 8 mm ✓
EPS 100 S 60+40 mm (Rigl)
Systémová deska 50 mm (Vyslyšel)
Beton 79 mm u nuly / 53 mm u vpusti (Doskočil),
hydroizolace + lepidlo + dlažba 13 mm (Doskočil)

Sprcha 1.21, 1×1 m, předpoklad
hydroizolace 8 mm ✓
EPS 100 S 60+40 mm (Rigl)
Systémová deska 50 mm (Vyslyšel)
Beton 79 mm u nuly / 66,5 mm u vpusti (Doskočil),
hydroizolace + lepidlo + dlažba 13 mm (Doskočil)
předpoklad, není ve výkazu

Sklad 1.18 — bez systémové desky
hydroizolace 8 mm ✓
EPS 150 S 100+40 mm (Rigl)
Litý beton 100 mm (Harvalík)
bez systémové desky a bez nášlapu

Hydroizolace 8 mm je hotová (✓). Tloušťky EPS a potěru jsou z podlaha-eps.xlsx.
Potěr lije Harvalík v celém domě, v koupelnách mimo sprchy a v celé spádované 1.20. Doskočil lije potěr jen ve sprše 1.07 a ve sprše 1×1 m v koupelně 1.21.
Předpoklad: sprcha garsonky je čtverec 1000×1000 mm v severozápadním rohu koupelny 1.21 (nejdál od dveří OP40 v jižní stěně). Ve výkazu ani v modelu sprcha není. Spád 1,25 % jako u sprchy 1.07, na 1,0 m tedy 12,5 mm. EPS 100 S 60+40 mm a potěr 79 mm u nuly / 66,5 mm u vpusti jsou předpoklad (výkaz má celou 1.21 jako EPS 60+60 a potěr 59 mm).
Garáž a 1.17: EPS 150 S, beton 100 mm. Výkaz říká ověřit EPS 150 se statikem (projekt měl XPS 80).
Sklad 1.18 je nevytápěný: bez systémové desky a bez nášlapu. Beton 100 mm je ve výkazu zástupná tloušťka.
Terasa ve výkazu skladeb není. Průchod 1.17–1.16 je bez stěny, obě plochy mají tutéž skladbu.